



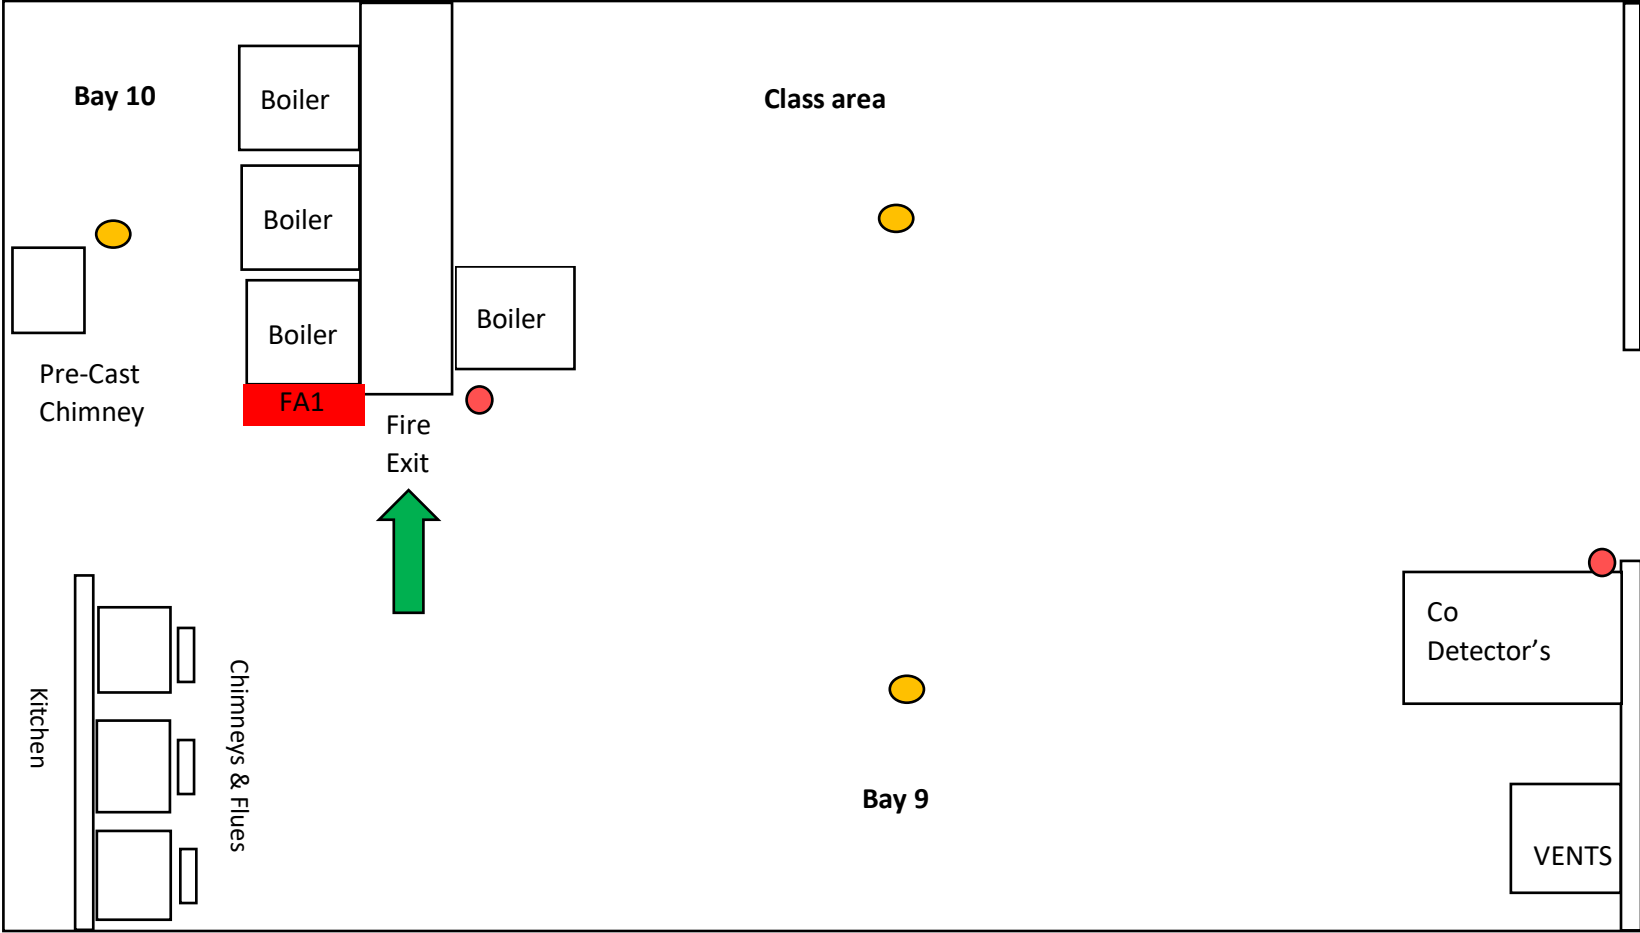

FC Training Academy - 285 -291 Wanstead Park Road MLP Floor Plan

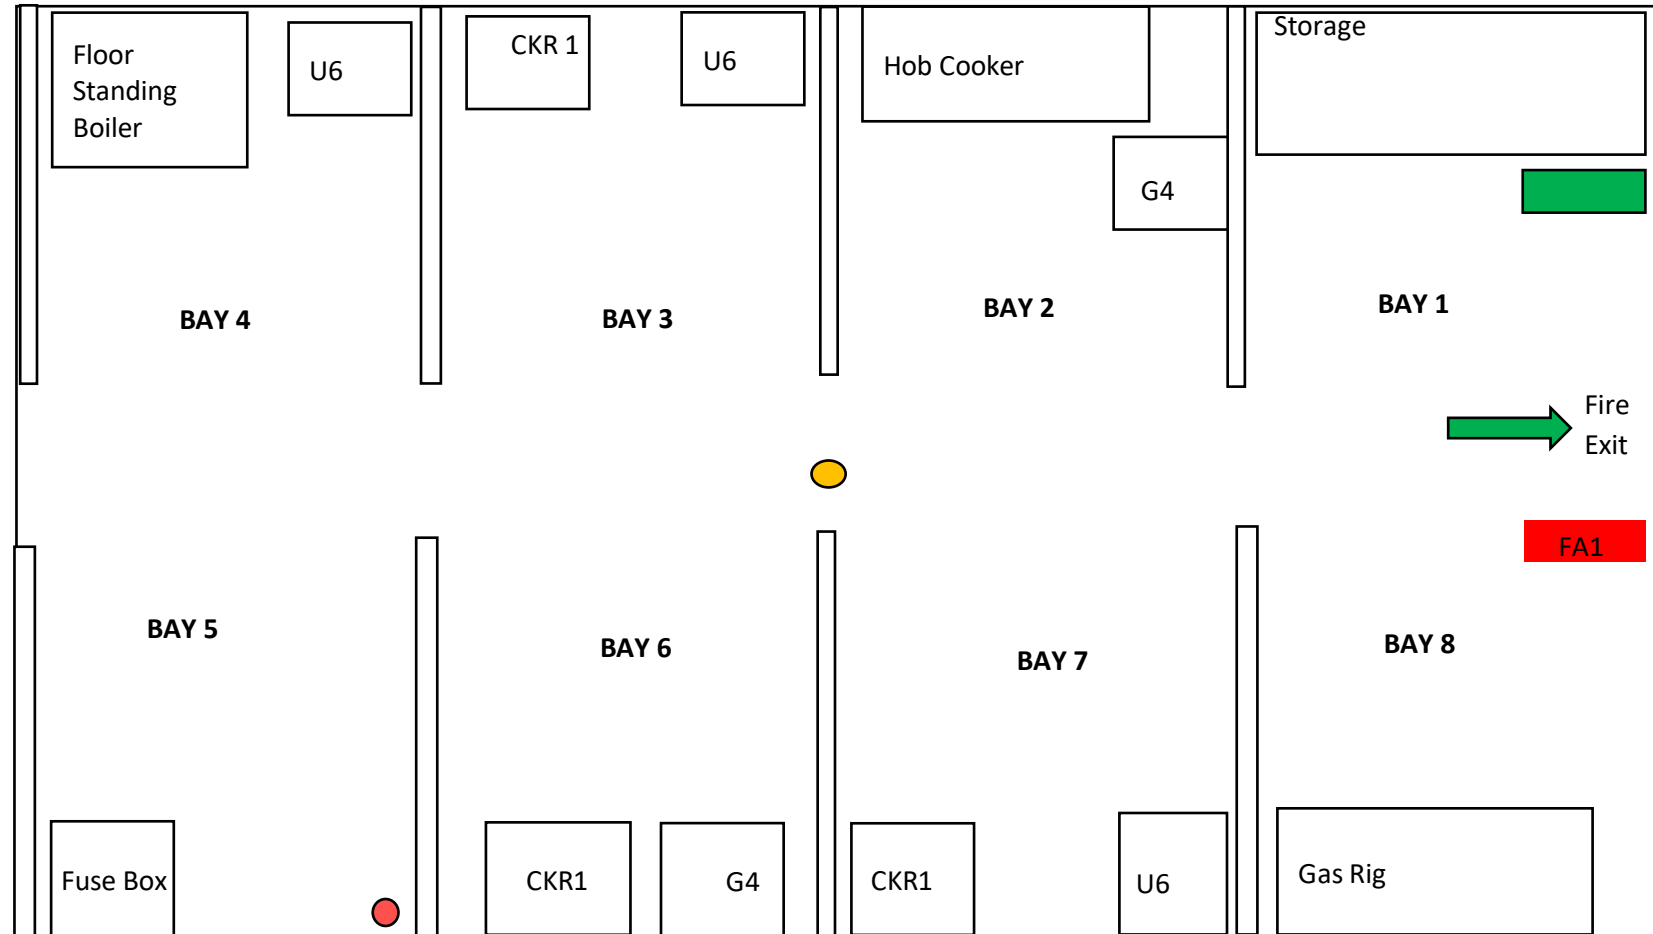

Key:



Fire Alarm



Emergency Stop Button

Date Created: 15.01.2025

Version 1

First Exit Route



First Aid Kit



Fire Extinguishers